



CONCEPT, NOT FOR FABRICATION

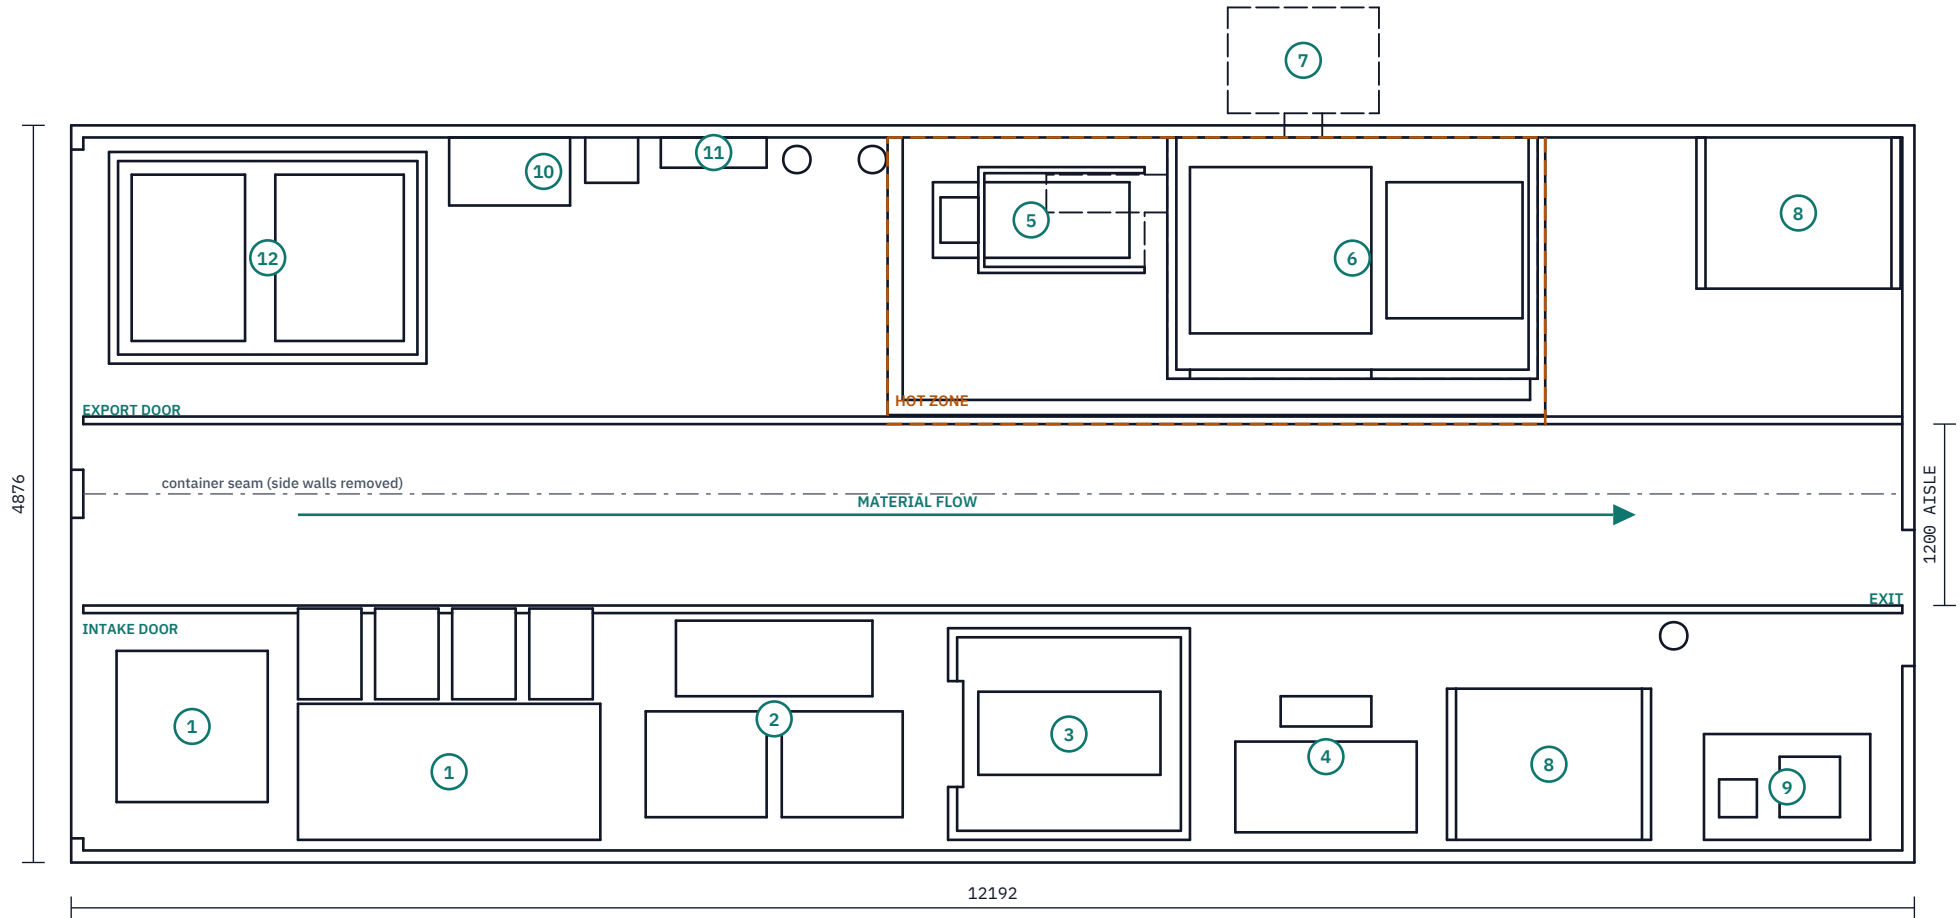

PLAN, SECTION AT 1.45 M

Scale 1:50; dashed: hoods, duct and fan above the cut

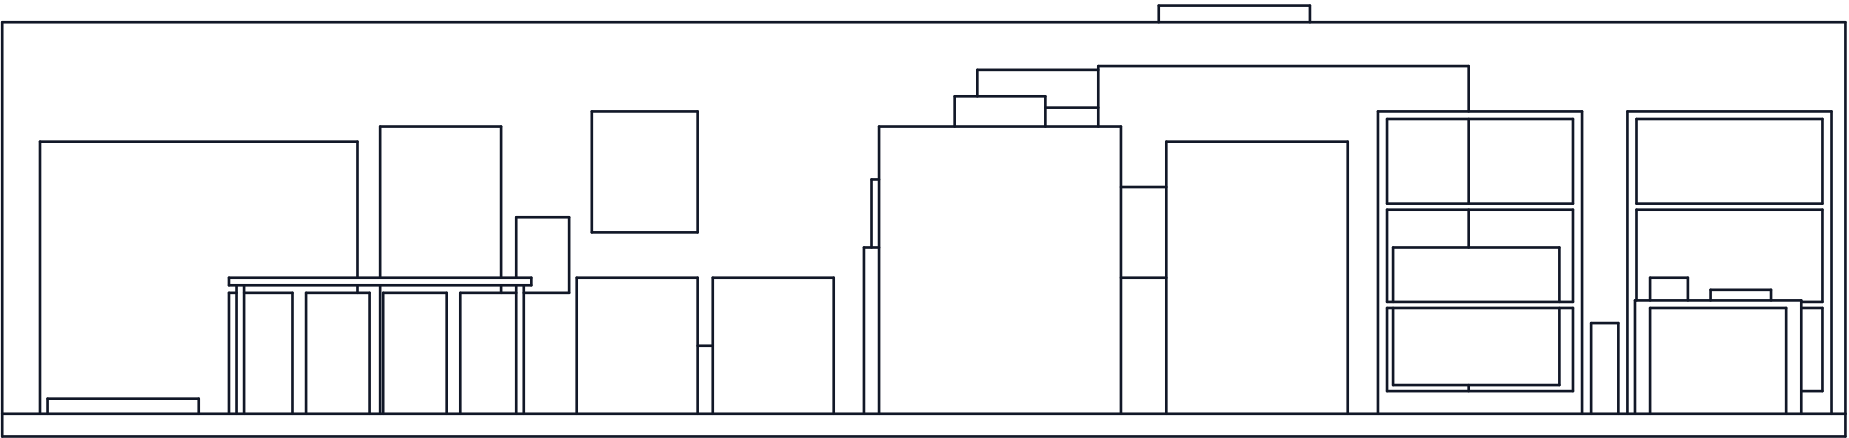

FRONT ELEVATION (FRONT WALL REMOVED)

Scale 1:50

REV	DESCRIPTION	DATE	BY
P1	Preliminary GA from the TRL 3 model (RFE-CAL-001)	2026-09-25	AC

ZONES (NUMBERS MATCH BOM/BOM.CSV)

- 1 Intake scale, sorting table, four bins
- 2 Wash tanks, float-sink, sediment trap
- 3 Shredder in lined acoustic enclosure
- 4 Drying rack (7.2 m2 trays) and fan
- 5 Extruder with barrel enclosure (hood B)
- 6 Sheet press and cooling press (booth A)
- 7 Hoods, 250 mm duct, fan and filter outside
- 8 Racking: bay 1 products, bay 2 flake
- 9 Passport and quality desk
- 10 PPE cabinet, eyewash, extinguishers
- 11 Electrical board, 230 V 40 A, interlock
- 12 Export and residue cage by export door
- 13 Two 40 ft containers, 12 192 x 4 876

KEY DATA (RFE-CAL-001)

59.4 m2 footprint; clear aisle 1.52 m (1.20 m painted)
Hot zone 1.0 m from stock; exits at both ends
100 kg input/shift: 32.3 kg products, 19.3 kg flake
Max demand 8.35 kW (36 A) with heater interlock
Hoods 0.5 m/s face: 0.57 m3/s at about 815 Pa
Shredder LEX 79 dB(A) enclosed (sound power assumed)
Not met: R1, R4, R8. At risk: R6, R12
Side wall removal needs a structural engineer
PRELIMINARY, NOT FOR FABRICATION

REFLOWECONOMY

Reference micro-factory, floor plan GA

DRAWING NO. RFE-DWG-001		REV P1	SHEET 1 of 1	SIZE ANSI B
SCALE 1:50	UNITS mm	PROJECTION 	DATE 2026-09-25	DRAWN Amish Chadha
MATERIAL / NOTES Layout only; equipment envelopes. See bom/bom.csv and RFE-CAL-001				
Licensed CERN-OHL-S-2.0 · Open Hardware Portfolio · amishchadha.com				Generated from cad/src; do not edit by hand