CONCEPT, NOT FOR FABRICATION

ReflowEconomy · github.com/BoujeeEnjinia1701/refloweconomy

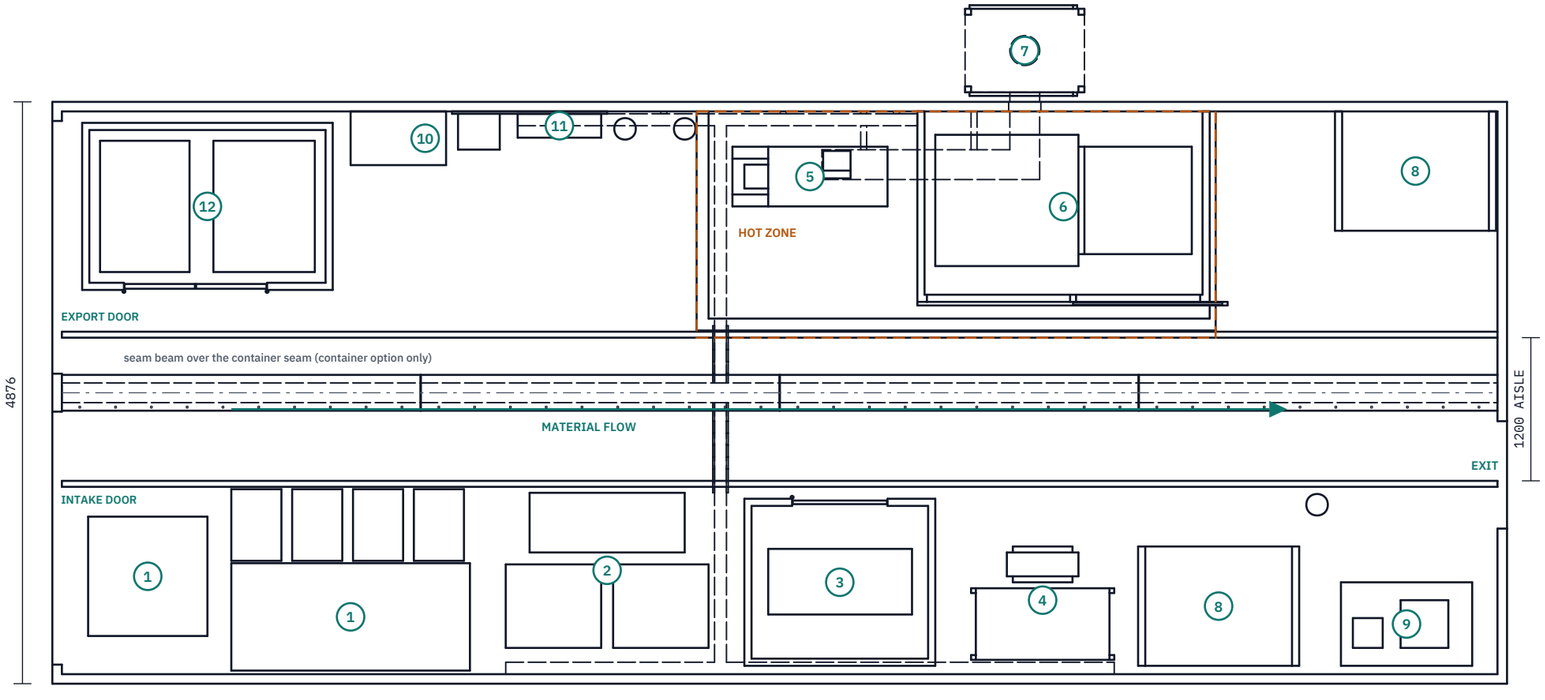

PLAN, SECTION AT 1.45 M

Scale 1:50; dashed: duct, fan, seam beam and cable tray above the cut

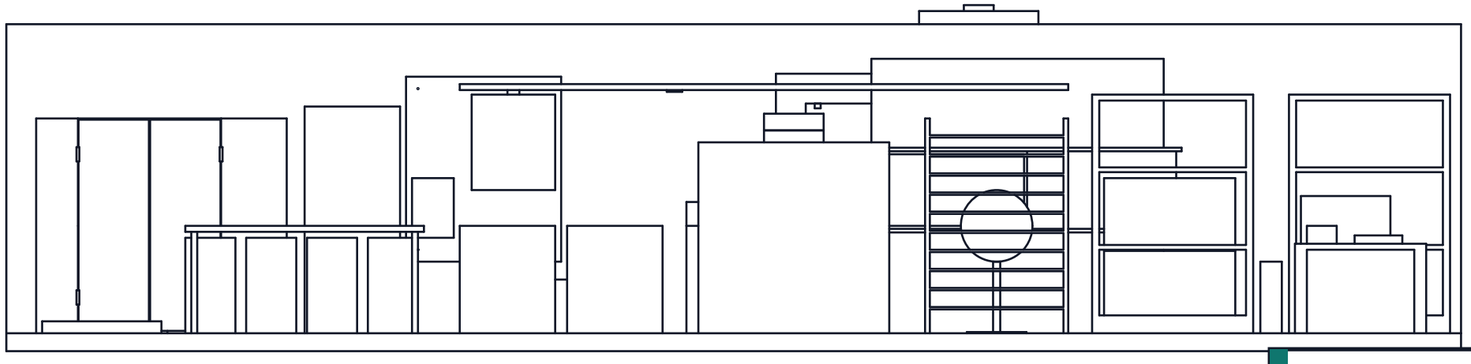

FRONT ELEVATION (FRONT WALL REMOVED; STACK CONTINUES 1 M ABOVE THE ROOF)

Scale 1:50

REV	DESCRIPTION	DATE	BY
P2	Notes: 1.5 kW fan, shed preferred (RFE-DDR-002)	2026-09-25	AC
P3	Design for construction (RFE-DDR-003): booth, duct, tray, seam beam	2026-09-30	AC
P4	Feed hood on the chute; self-closing hinges; padded tray crossing	2026-10-02	AC
P5	120 mm feed slot; supply note; PR numbers	2026-10-25	AC

ZONES (NUMBERS MATCH BOM/BOM.CSV)

1 Intake scale, sorting table, four bins
2 Wash tanks, float-sink, sediment trap
3 Shredder in lined acoustic enclosure
4 Drying rack (7.2 m2 trays) and fan
5 Extruder with barrel enclosure (hood B)
6 Sheet press and cooling press (booth A)
7 Hoods, sash, 250 mm duct, 1.5 kW fan on a stand
8 Racking: bay 1 products, bay 2 flake
9 Passport and quality desk
10 PPE cabinet, eyewash, extinguishers
11 Board on backboard, interlock, cable tray
12 Export and residue cage by export door
13 Shed preferred, or two 40 ft boxes with seam beam

KEY DATA (RFE-CAL-001)

59.4 m2 footprint; clear aisle 1.57 m (1.20 m painted)
Hot zone 1.0 m from stock; exits at both ends
100 kg input/shift: 32.3 kg products, 19.3 kg flake
Block A 55 A on 40 A single-phase: supply open (D1)
Hoods 0.5 m/s face: 0.57 m3/s at about 815 Pa
LEX 79 dB(A) enclosed; reach 1.06 m via 120 mm slot
Not met: PR-001, 004, 008, 017. At risk: PR-006, 012
Seam beam and side walls: structural engineer only
Headroom 2.02 m under the padded tray crossing
PRELIMINARY, NOT FOR FABRICATION

REFLOWECONOMY

github.com/BoujeeEnjinia1701/refloweconomy

Reference micro-factory, floor plan GA

DRAWING NO.	REV	SHEET	SIZE
RFE-DWG-001	P5	1 of 1	ANSI B

SCALE	UNITS	PROJECTION	DATE	DRAWN
1:50	mm		2026-10-25	Amish Chadha

MATERIAL / NOTES

Layout only; equipment envelopes. See bom/bom.csv and RFE-CAL-001

Licensed CERN-OHL-S-2.0 · Design Molecule Lab · designmolecule.com

Generated from cad/src; do not edit by hand